

ALT-1

대 지 조 서

대 지 위 치	부천시 원미구 역곡동 63-9, 10번지		
대 지 면 적	347.9 M2 (105.3평)		
지 역 . 지 구	제2종일반주거지역		
건 축 주		주 소	

공 지 비 율 표

건 축 면 적	207.91
연 면 적	916.33 (277.18평)
건 폐 율	207.91 / 347.9 x 100 = 59.76 %
용 적 율	676.62 / 347.9 x 100 = 194.49 %
주 차 대 수	법정 : 11 x 1.0 + 121.84 / 134 = 12대
	계획 : 자주식 12대
도 로 현 황	8, 6M 막다른도로에 접함.

건 물 면 적 표

층 별		101동	소 계	비 고
지상	1 층	근린생활시설 / 지하 주차장	239.71	
	소 계		239.71	
지상	1 층	근린생활시설 / 피로티 주차장	48.65	
	2 층	다세대주택-3세대	172.54	
	3 층	다세대주택-3세대	172.54	
	4 층	다세대주택-3세대	145.31	
	5 층	다세대주택-2세대	137.58	
	소 계	다세대주택-11세대	676.62	
합 계		근린생활시설-2호 다세대주택-11세대	916.33	

 **도움**

ARCHITECTS & ENGINEERS
건축사사무소
TEL : (031) 443 - 0341
FAX : (031) 443 - 0342
MOBILE : 010 - 3009 - 0341
E-mail : doulum-h@hanmail.net

공 사 명
PROJECT TITLE
부천시 역곡동
63-9, 10번지
다세대주택 신축공사

기 사
NOTE

건축설계
ARCHITECTURAL DESIGNED BY

구조설계
STRUCTURAL DESIGNED BY

설비설계
MECHANICAL DESIGNED BY

전기설계
ELECTRICAL DESIGNED BY

설 계
DESIGNED BY

제 도
DRAWN BY

심 사
CHECKED BY

심 사
CHECKED BY

승 인
APPROVED BY

승 인
APPROVED BY 건축사: 허재선

날 짜
DATE 2026.

축 척
SCALE A3 : 1 /

일련번호
SHEET NO.

파일번호
FILE NO.

도 면 명
DRAWING TITLE

도면번호
DRAWING NO.



ARCHITECTS & ENGINEERS
건축사사무소

TEL : (031) 443 - 0341
FAX : (031) 443 - 0342
MOBILE : 010 - 3009 - 0341

E-mail : doun-h@hanmail.net

공사명
PROJECT TITLE

부천시 역곡동
63-9, 10번지
다세대주택 신축공사

기
NOTE

건축설계
ARCHITECTURAL DESIGNED BY

구조설계
STRUCTURAL DESIGNED BY

설비설계
MECHANICAL DESIGNED BY

전기설계
ELECTRICAL DESIGNED BY

설
DESIGNED BY

제
DRAWN BY

심
CHECKED BY

심
CHECKED BY

승
APPROVED BY

승
APPROVED BY 건축사: 허재선

날
DATE 2026.



축
SCALE A3 : 1 /

일련번호
SHEET NO.


파일번호
FILE NO.

도
DRAWING TITLE

도면번호
DRAWING NO.

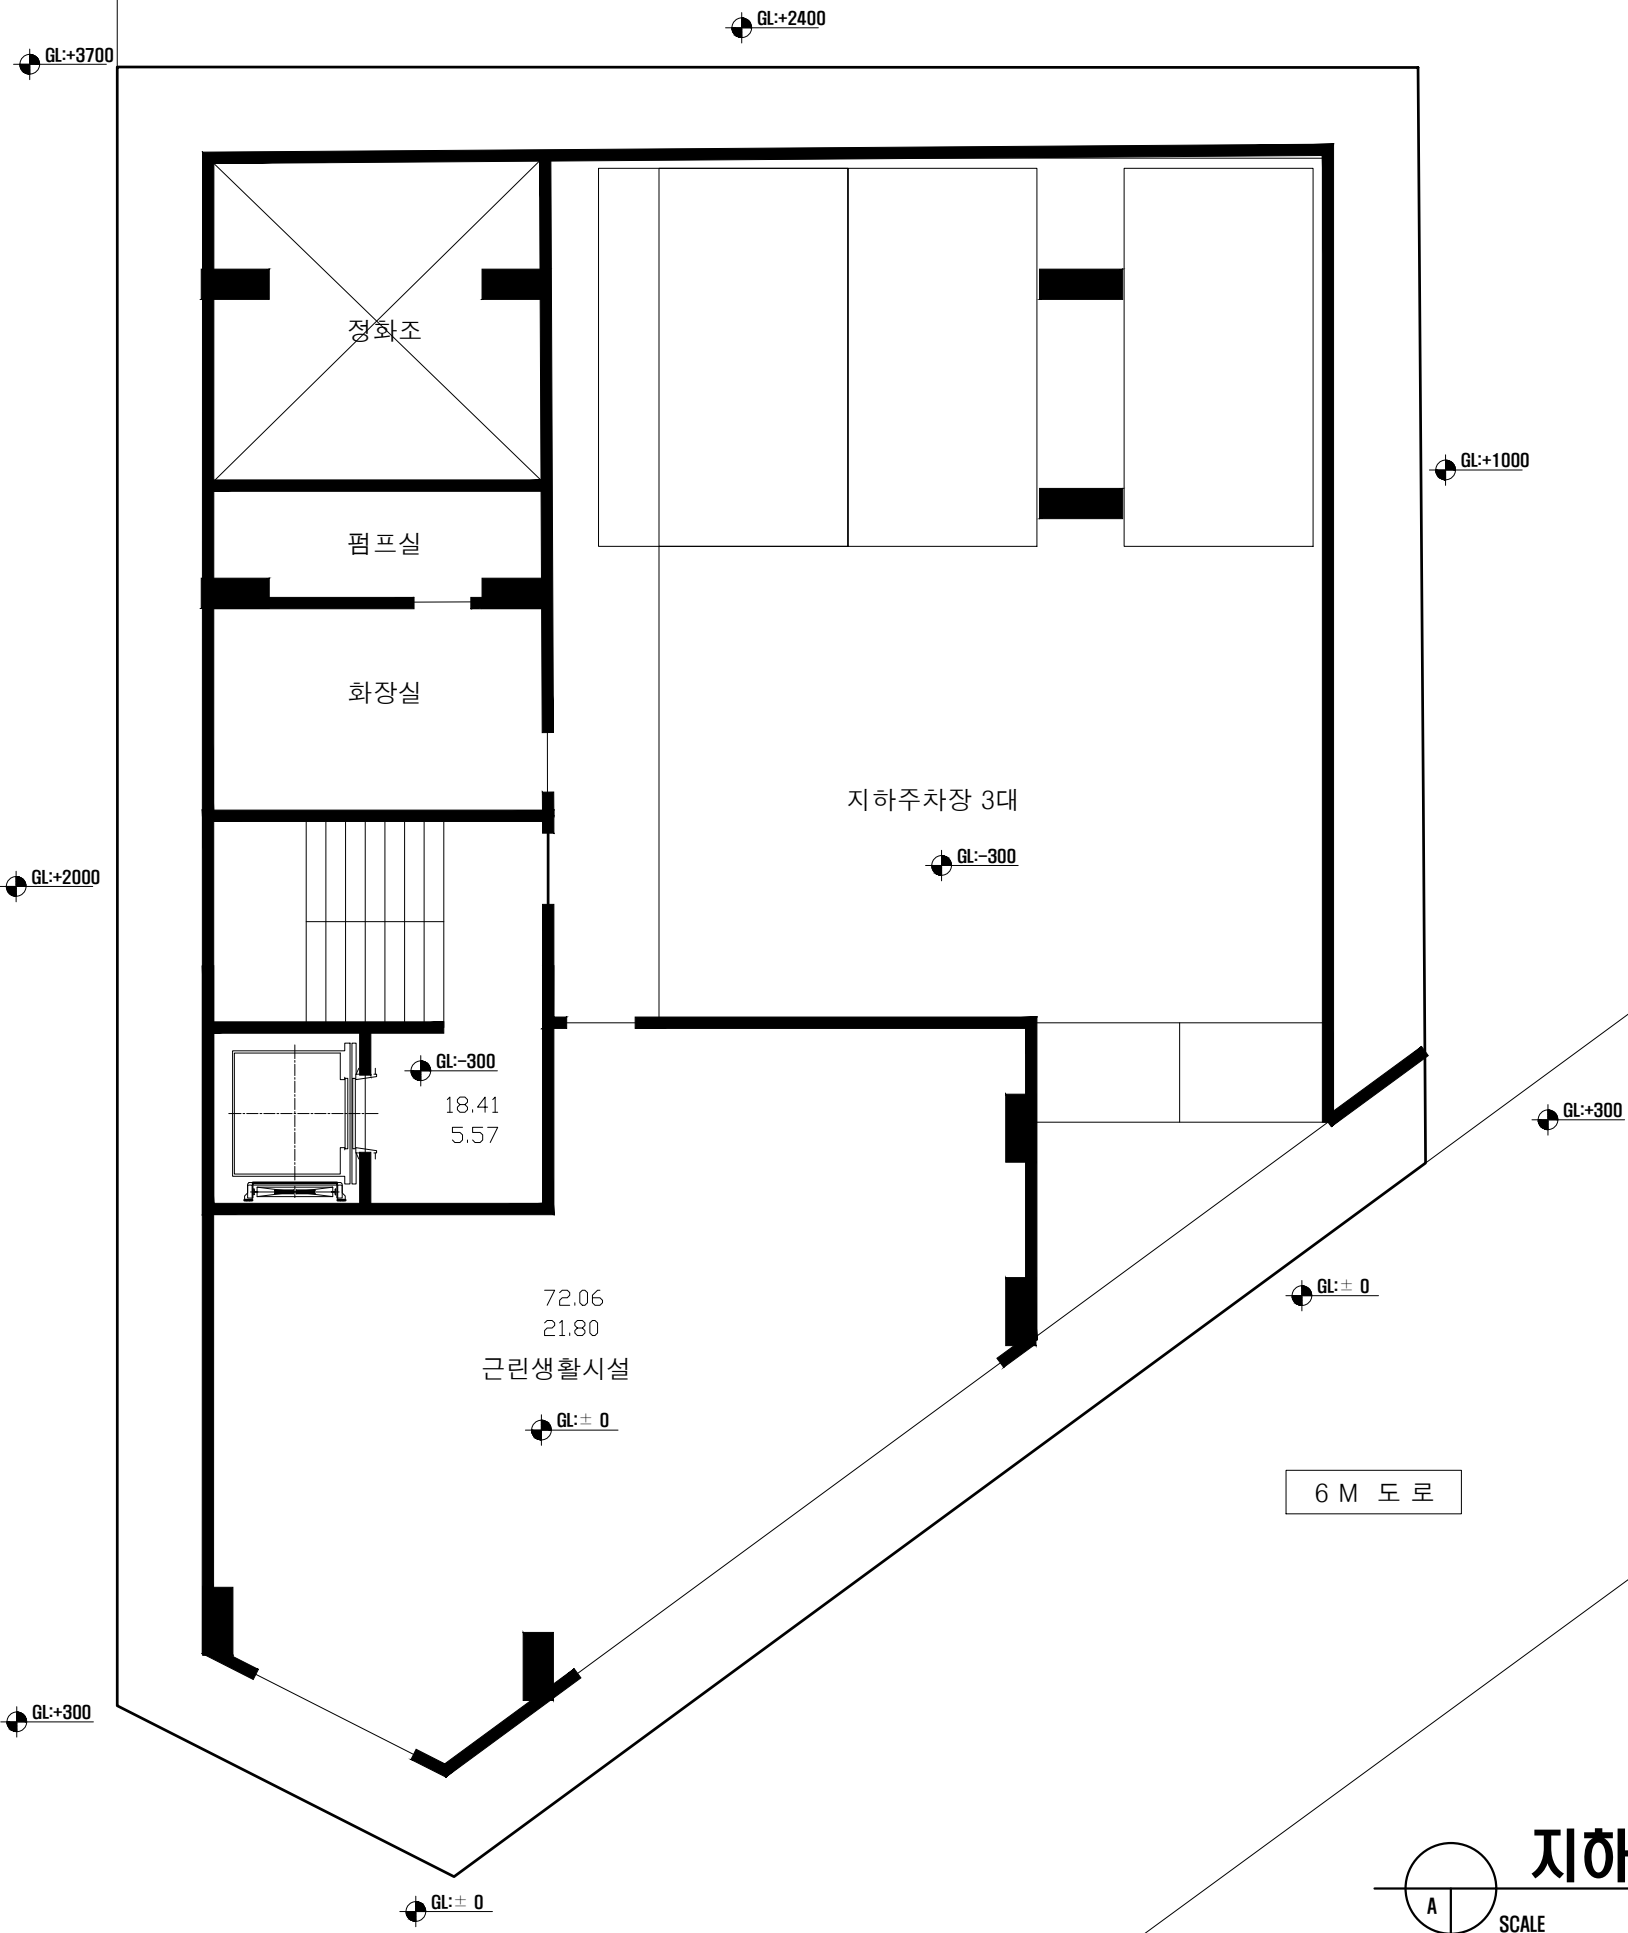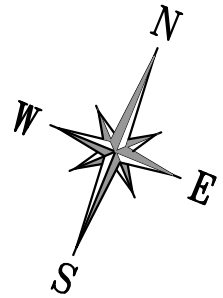


지하1층 평면도

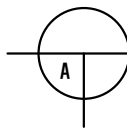

SCALE

= 1 / 100

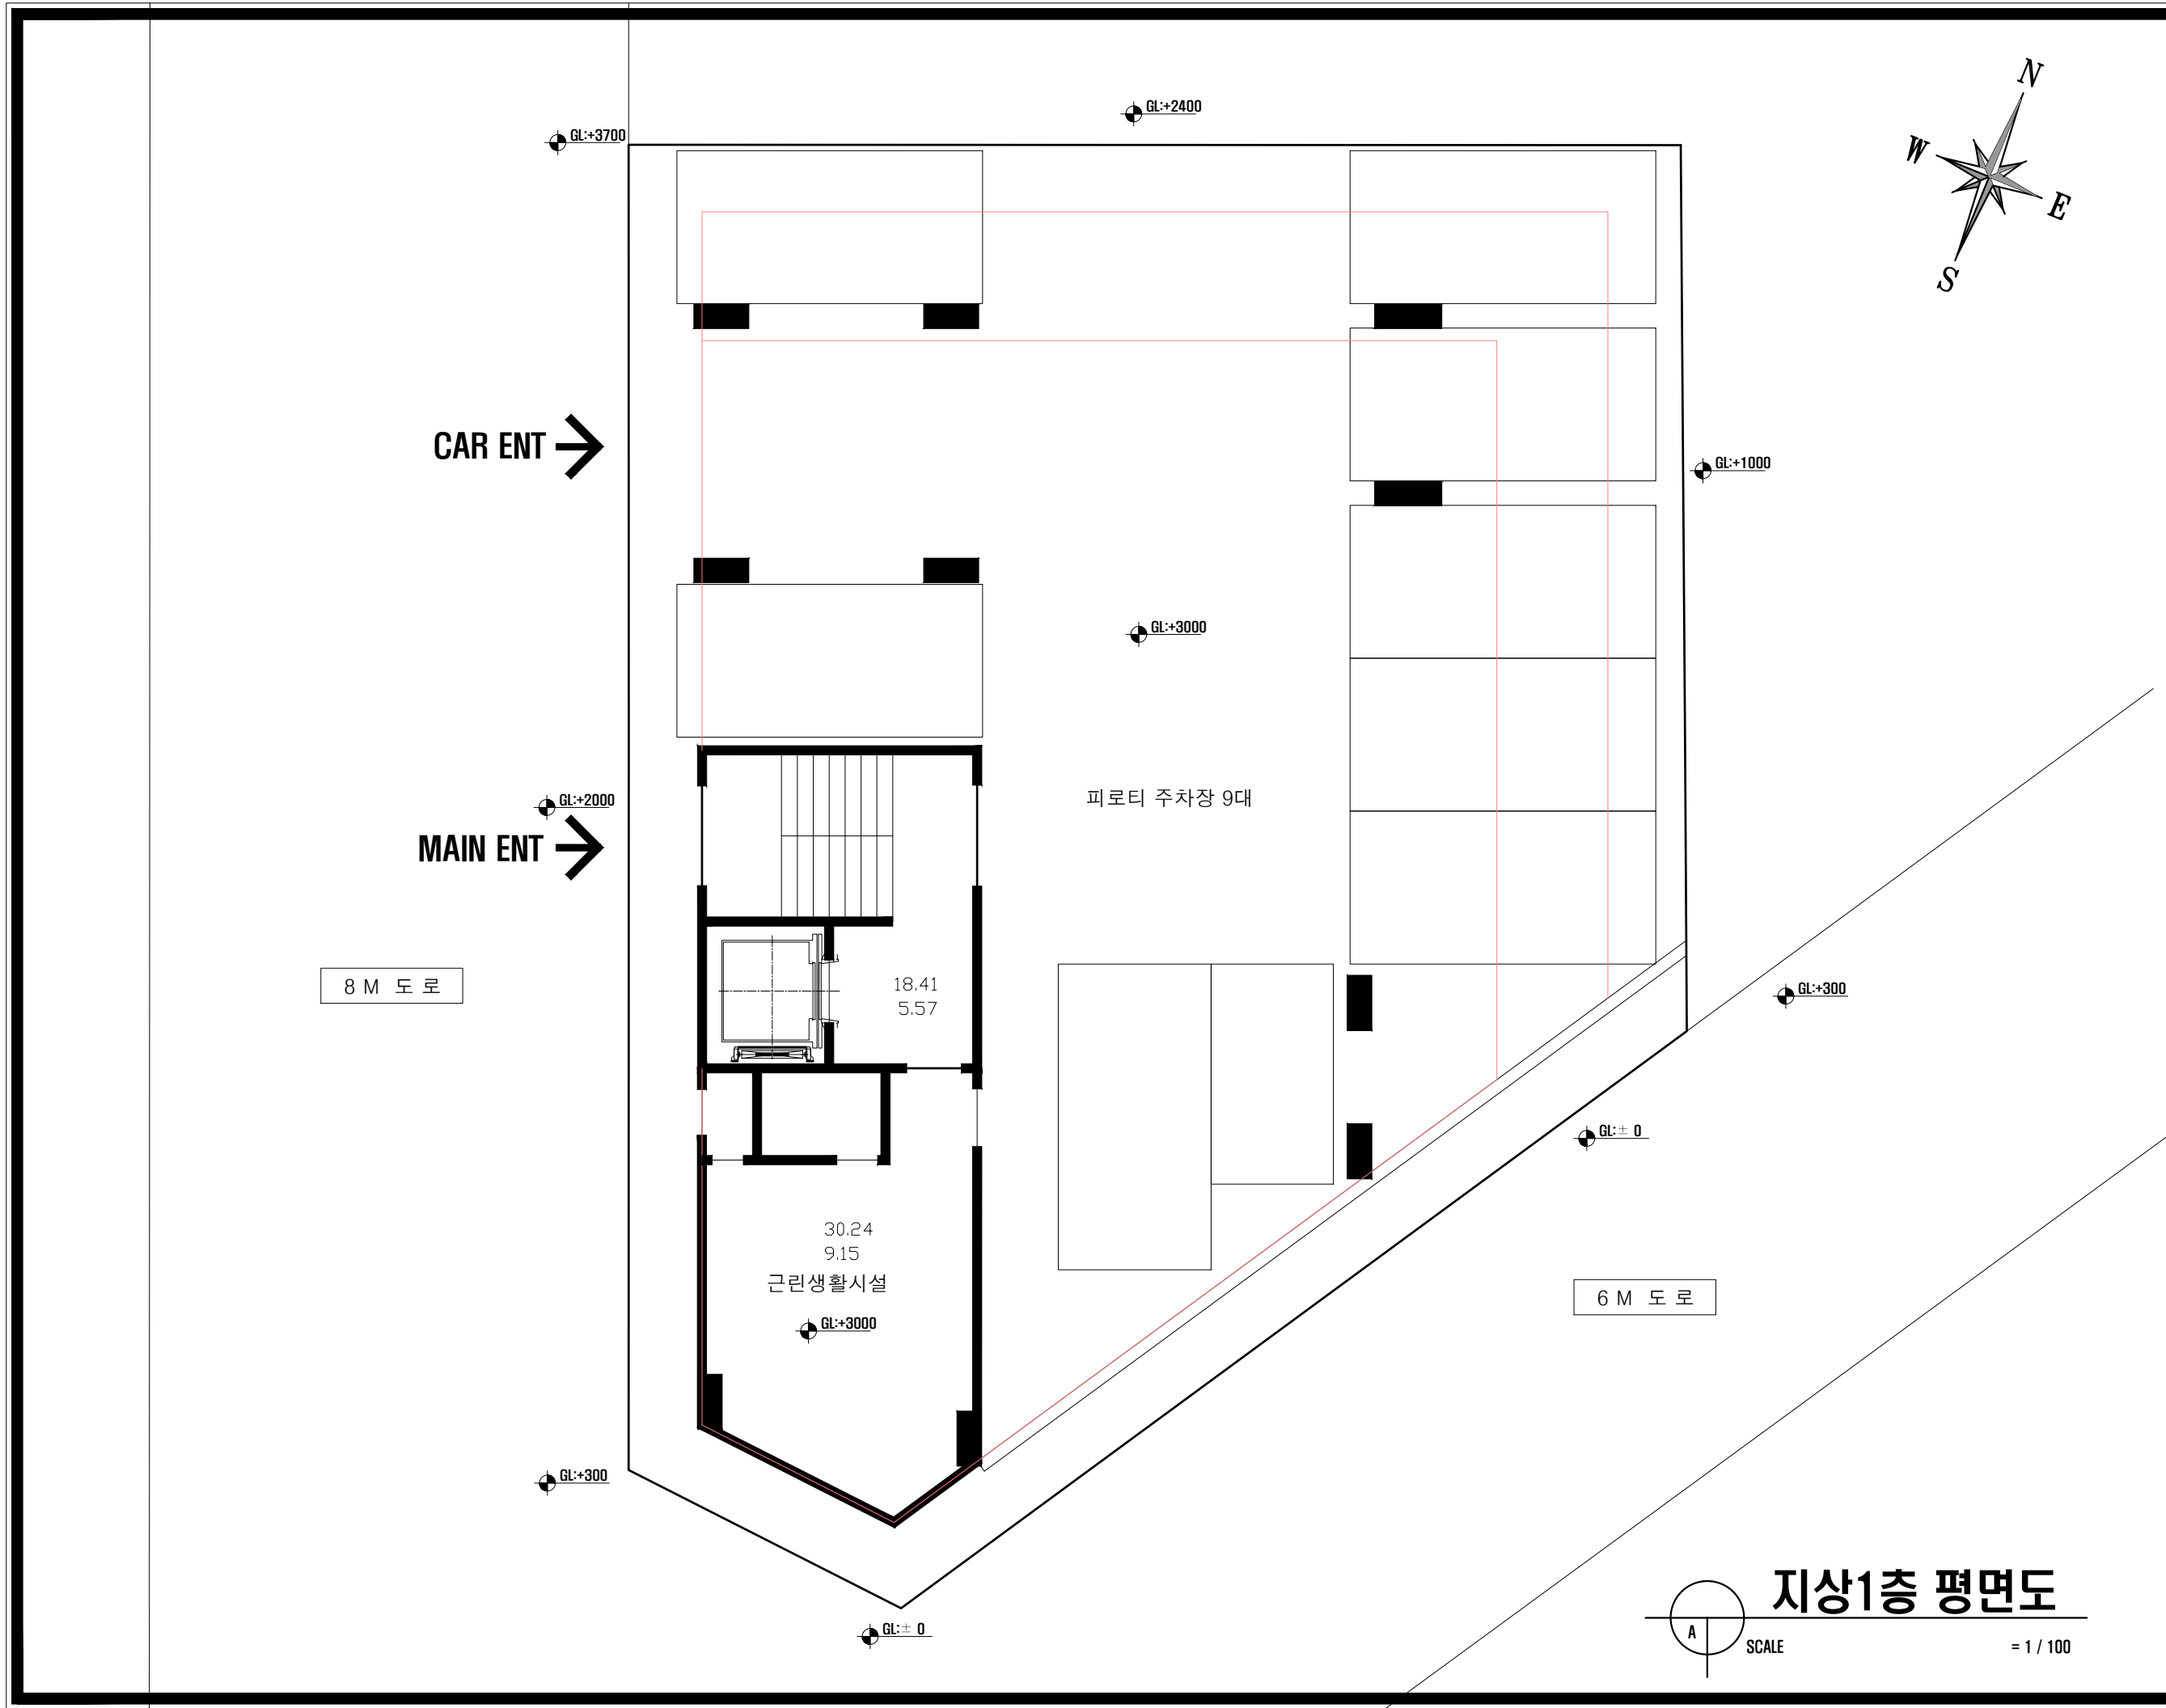





도움

ARCHITECTS & ENGINEERS
건축사사무소
TEL : (031) 443 - 0341
FAX : (031) 443 - 0342
MOBILE : 010 - 3009 - 0341
E-mail : doun-h@hanmail.net

공사명
PROJECT TITLE
부천시 역곡동
63-9, 10번지
다세대주택 신축공사

기
사
NOTE

건축설계 ARCHITECTURAL DESIGNED BY	
구조설계 STRUCTURAL DESIGNED BY	
설비설계 MECHANICAL DESIGNED BY	
전기설계 ELECTRICAL DESIGNED BY	
설 계 DESIGNED BY	
제 도 DRAWN BY	
심 사 CHECKED BY	
심 사 CHECKED BY	
승 인 APPROVED BY	
승 인 APPROVED BY 건축사: 허재선	
날 짜 DATE	2026.
축 척 SCALE	A3 : 1 /
일련번호 SHEET NO.	
파일번호 FILE NO.	
도 면 명 DRAWING TITLE	
도면번호 DRAWING NO.	

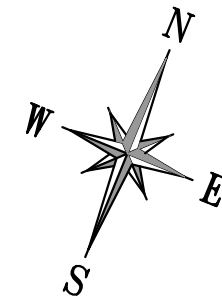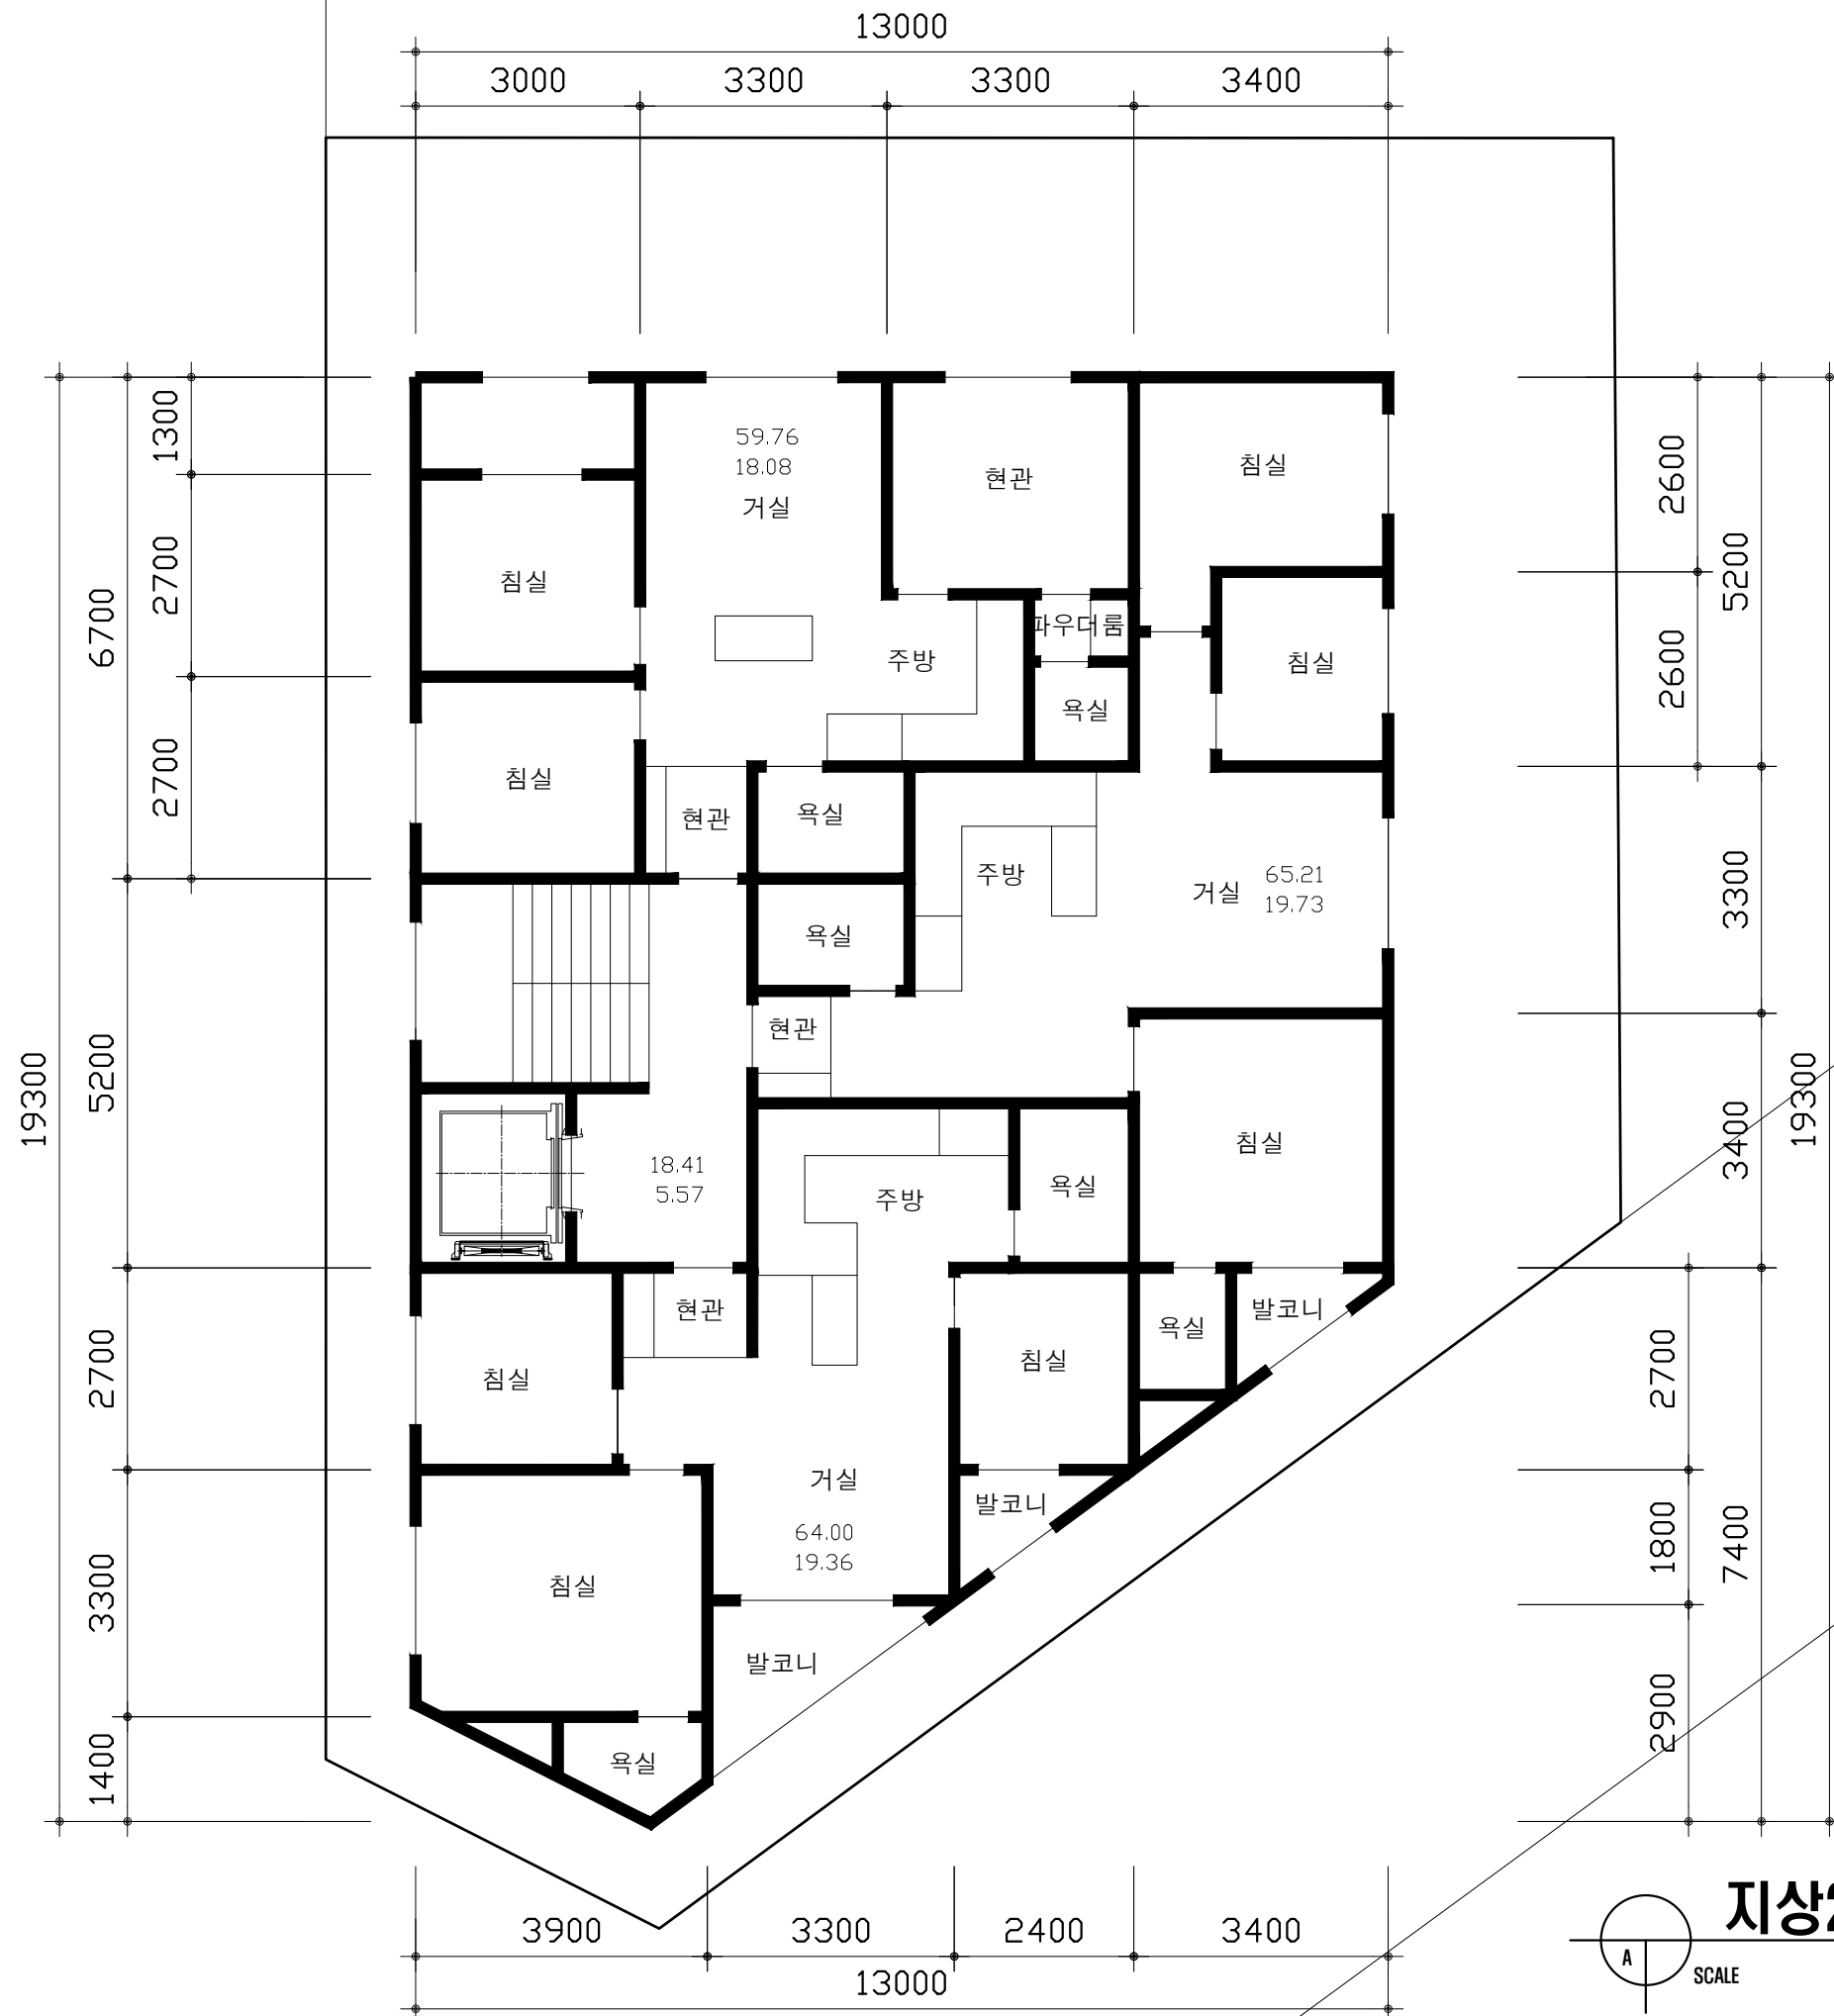

ARCHITECTS & ENGINEERS
건축사사무소

TEL : (031) 443 - 0341
FAX : (031) 443 - 0342
MOBILE : 010 - 3009 - 0341

E-mail : doom-h@hanmail.net

공사명
PROJECT TITLE

부천시 역곡동
63-9, 10번지
다세대주택 신축공사

기
NOTE

건축설계
ARCHITECTURAL DESIGNED BY

구조설계
STRUCTURAL DESIGNED BY

설비설계
MECHANICAL DESIGNED BY

전기설계
ELECTRICAL DESIGNED BY

설
DESIGNED BY

제
DRAWN BY

심
CHECKED BY

심
CHECKED BY

승
APPROVED BY

승
APPROVED BY 건축사: 허재선

날
DATE 2026.

축
SCALE A3 : 1 /


일련번호
SHEET NO.

파일번호
FILE NO.

도
DRAWING TITLE

도
DRAWING NO.

지상2~3층 평면도

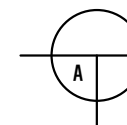

SCALE

= 1 / 100



ARCHITECTS & ENGINEERS
건축사사무소

TEL : (031) 443 - 0341
FAX : (031) 443 - 0342
MOBILE : 010 - 3009 - 0341

E-mail : doom-h@hanmail.net

공사명
PROJECT TITLE
부천시 역곡동
63-9, 10번지
다세대주택 신축공사

기
NOTE

건축설계
ARCHITECTURAL DESIGNED BY

구조설계
STRUCTURAL DESIGNED BY

설비설계
MECHANICAL DESIGNED BY

전기설계
ELECTRICAL DESIGNED BY

설
DESIGNED BY

제
DRAWN BY

심
CHECKED BY

심
CHECKED BY

승
APPROVED BY

승
APPROVED BY 건축사: 허재선

날
DATE 2026.



축
SCALE A3 : 1 /

일련번호
SHEET NO.

파일번호
FILE NO.

도
DRAWING TITLE

도
DRAWING NO.

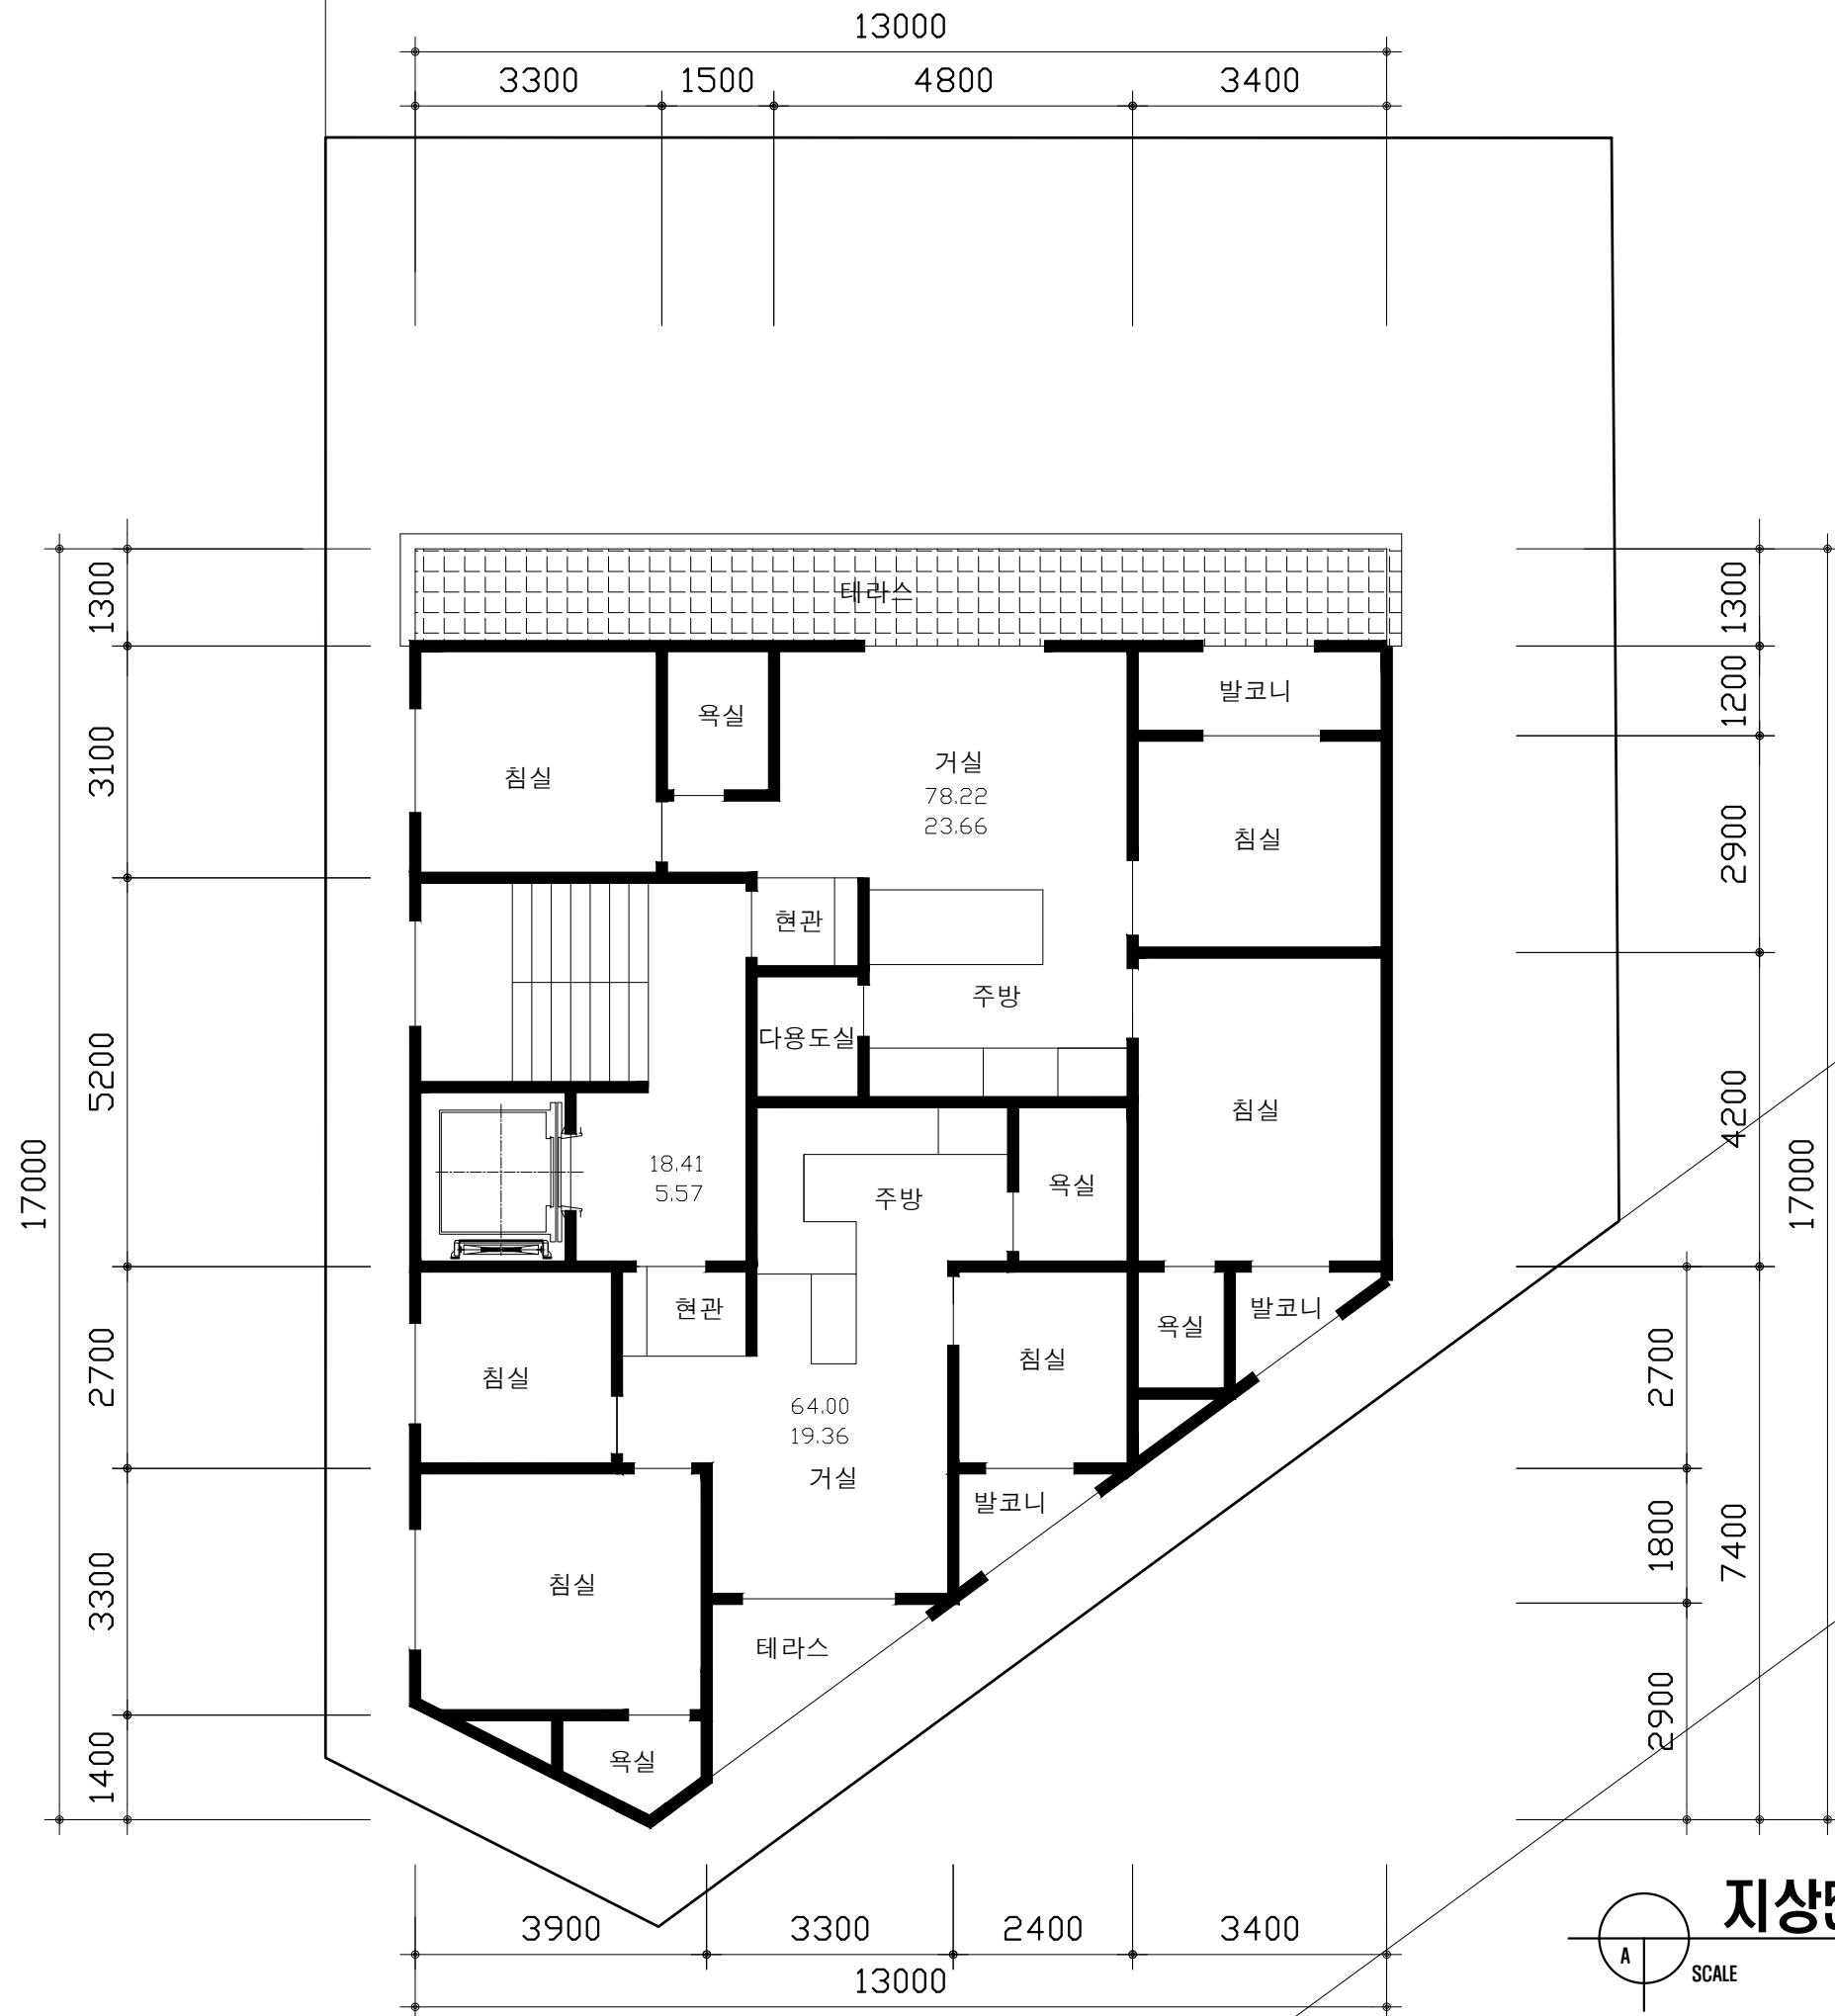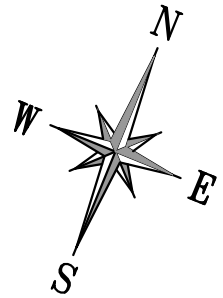

지상5층 평면도

= 1 / 100