



ARCHITECTS & ENGINEERS
건축사사무소

TEL : (031) 443 - 0341
FAX : (031) 443 - 0342
MOBILE : 010 - 3009 - 0341

E-mail : doun-h@hanmail.net

공사명
PROJECT TITLE
수원시 팔달구 매산로3가
68-4번지
오피스텔 신축공사

기
사
NOTE

건축설계
ARCHITECTURAL DESIGNED BY

구조설계
STRUCTURAL DESIGNED BY

설비설계
MECHANICAL DESIGNED BY

전기설계
ELECTRICAL DESIGNED BY

설
계
DESIGNED BY

제
도
DRAWN BY

심
사
CHECKED BY

심
사
CHECKED BY

승
인
APPROVED BY

승
인
APPROVED BY 건축사: 허재선

날
짜
DATE 2026.




축
척
SCALE A3 : 1 /

일련번호
SHEET NO.

파일번호
FILE NO.

도
면
명
DRAWING TITLE

도면번호
DRAWING NO.

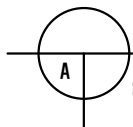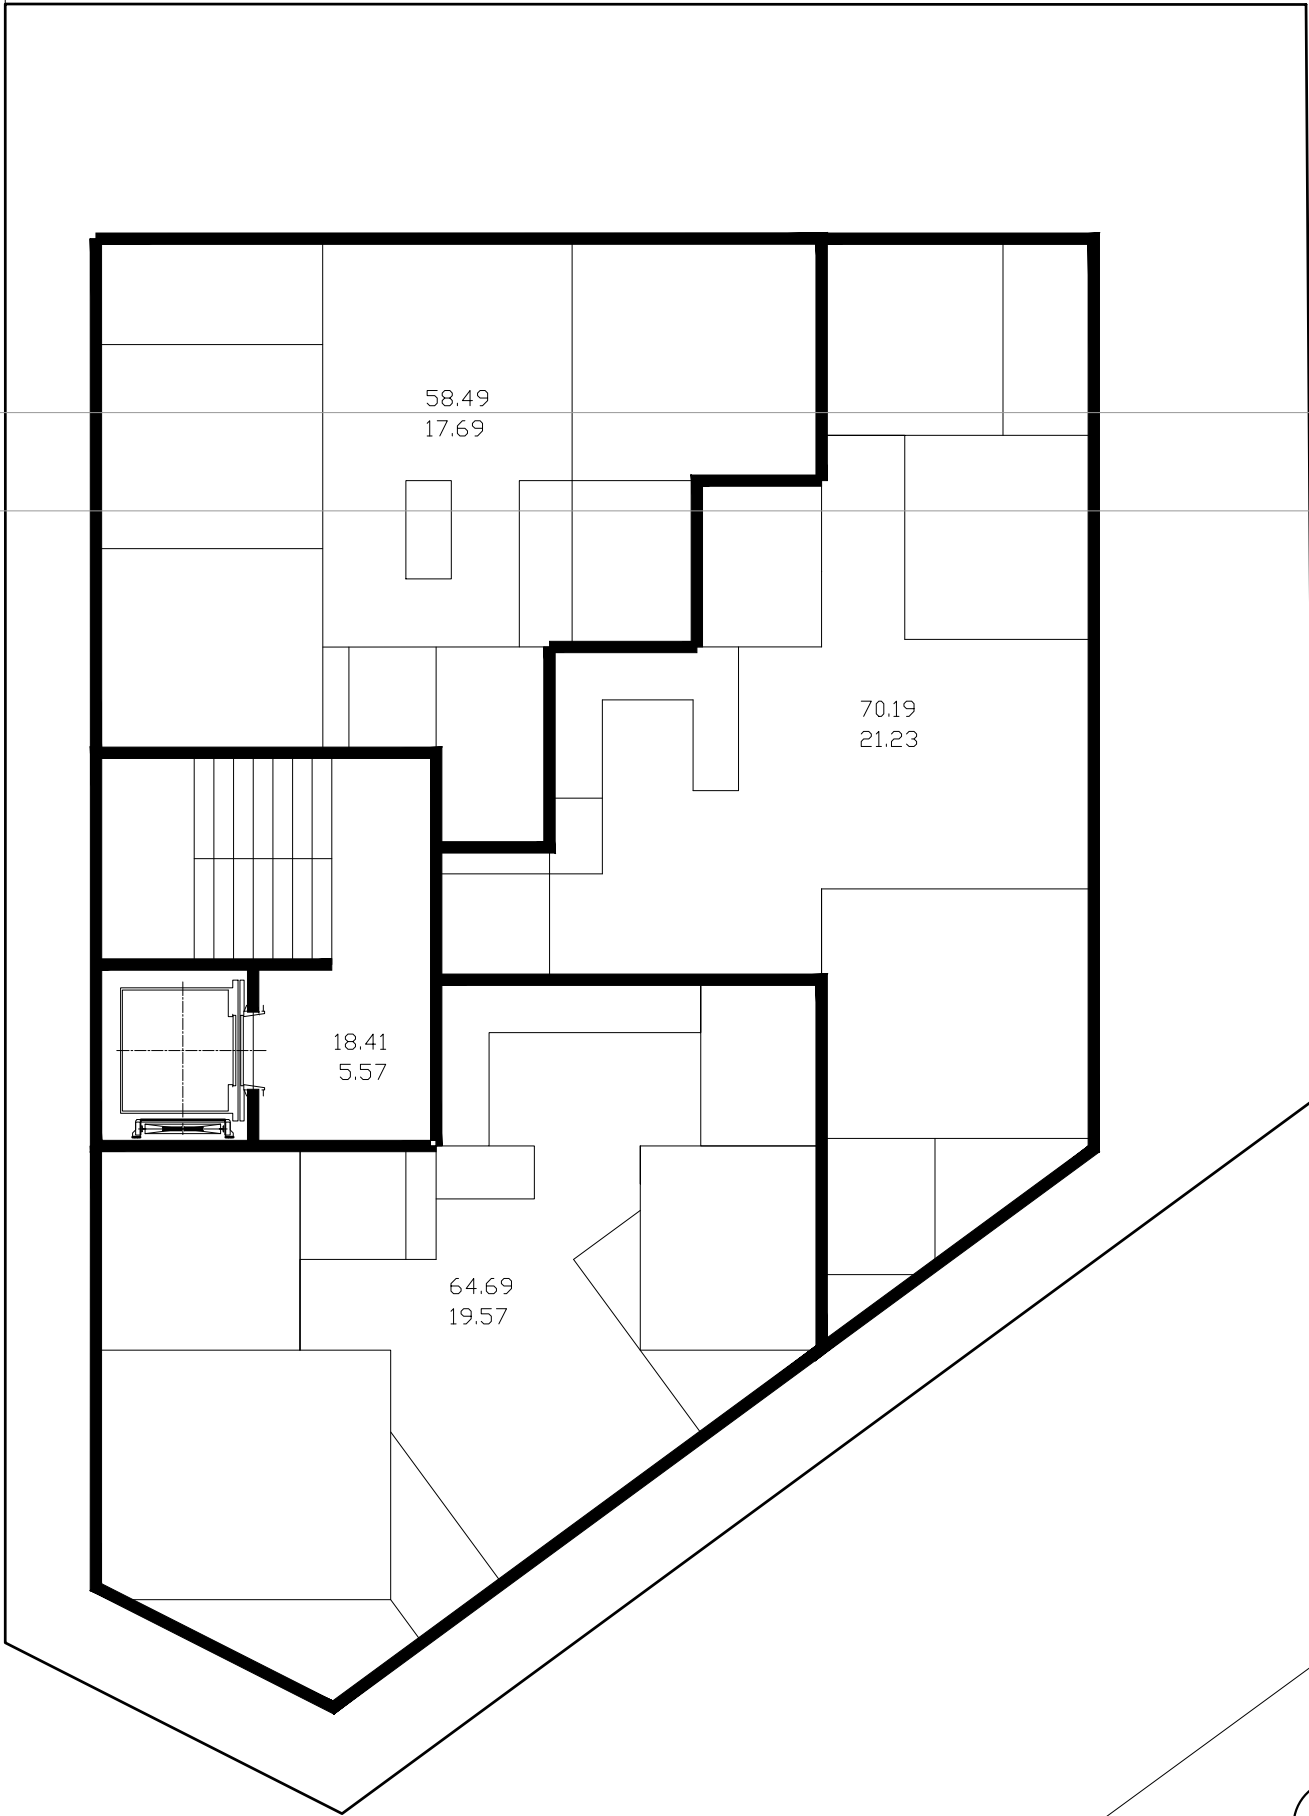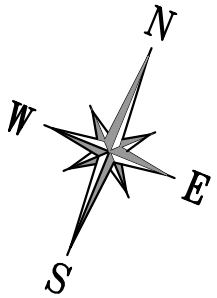

지상2~3층 평면도

SCALE

= 1 / 100